



vernier test fixture

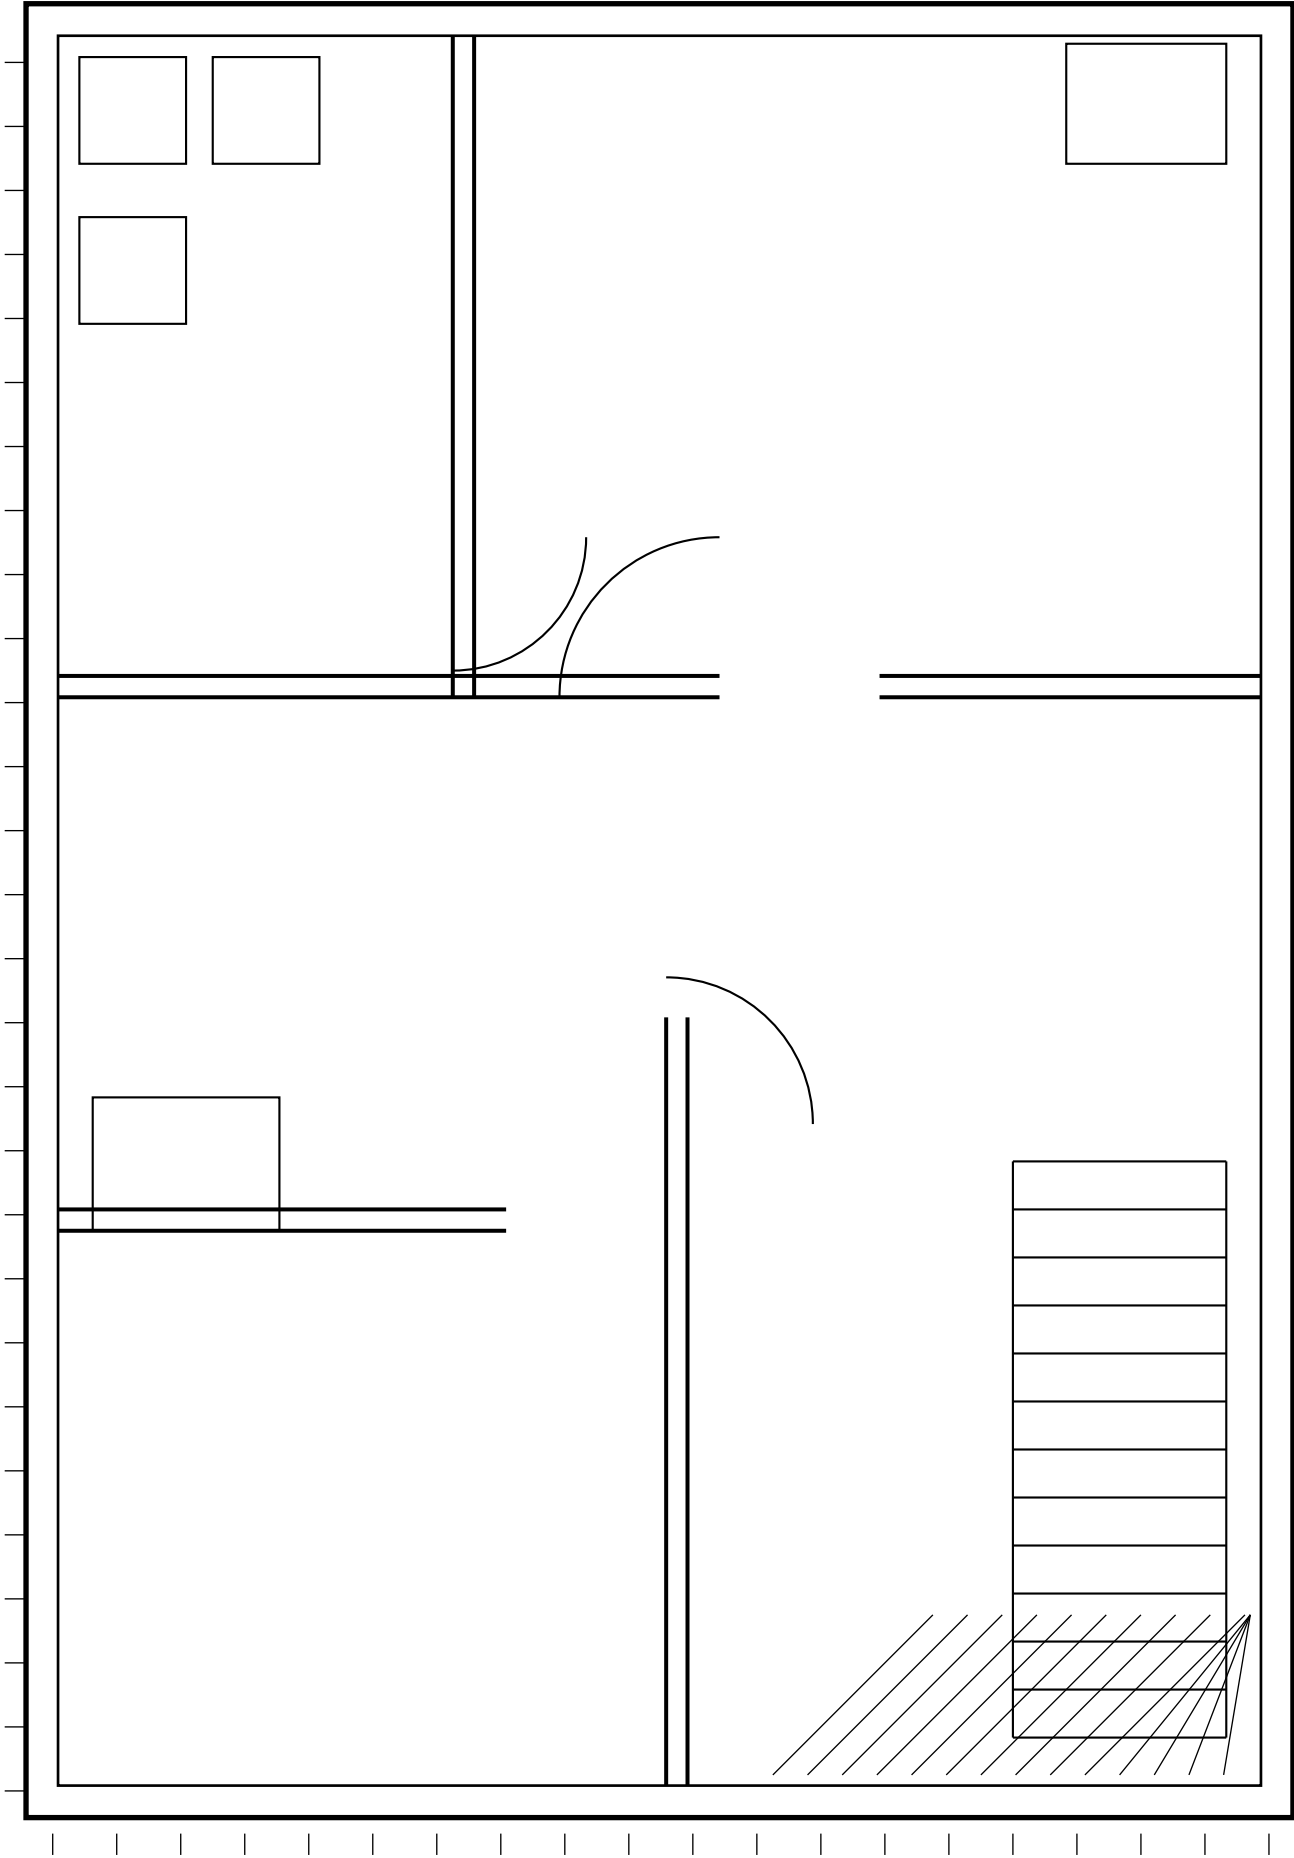

SAMPLE HOUSE - GROUND FLOOR

Synthetic fixture. Not a real building. 1:50 at A4.

vernier test fixture

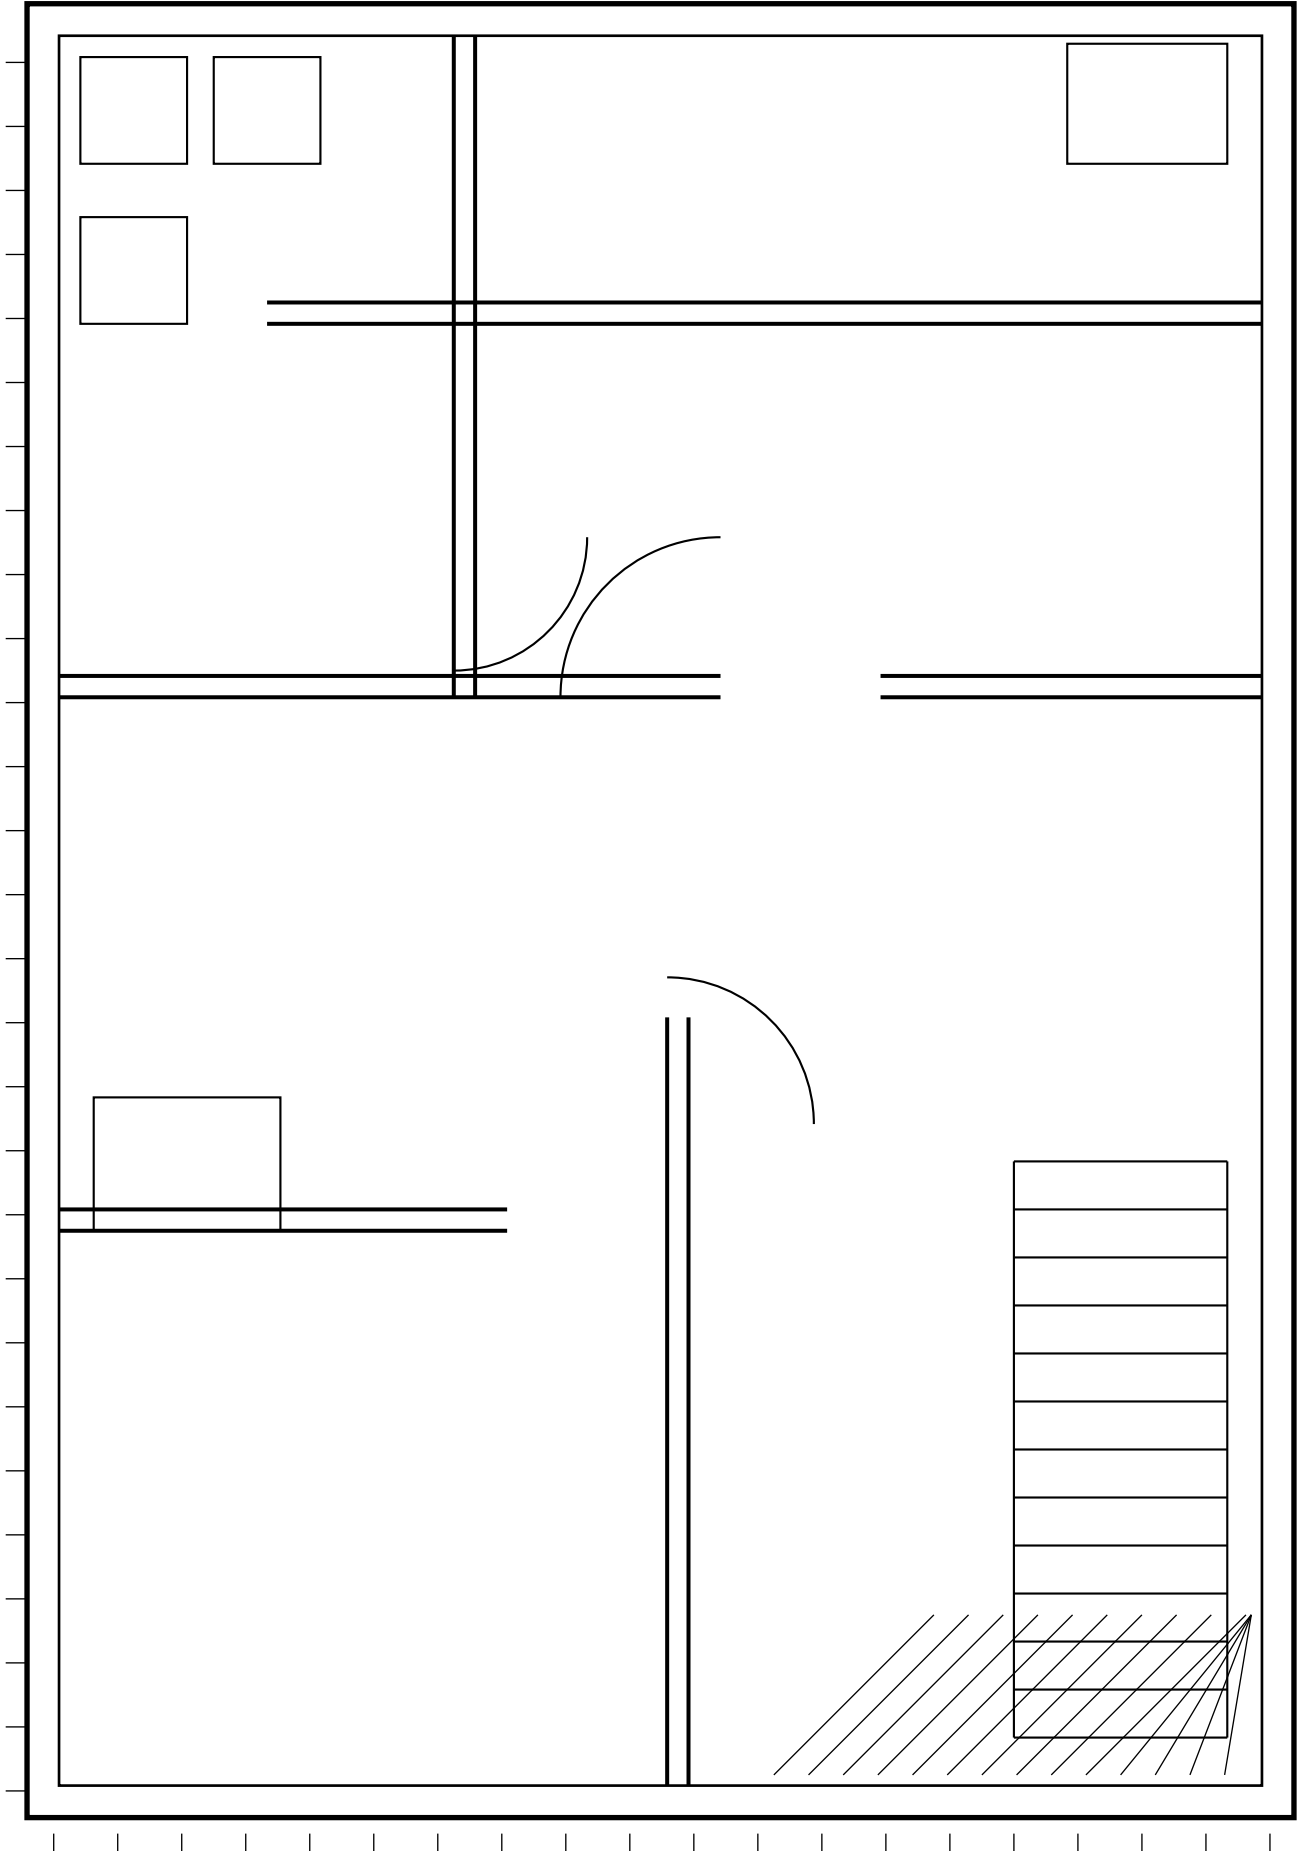

SAMPLE HOUSE - FIRST FLOOR

Synthetic fixture. Not a real building. 1:50 at A4.